


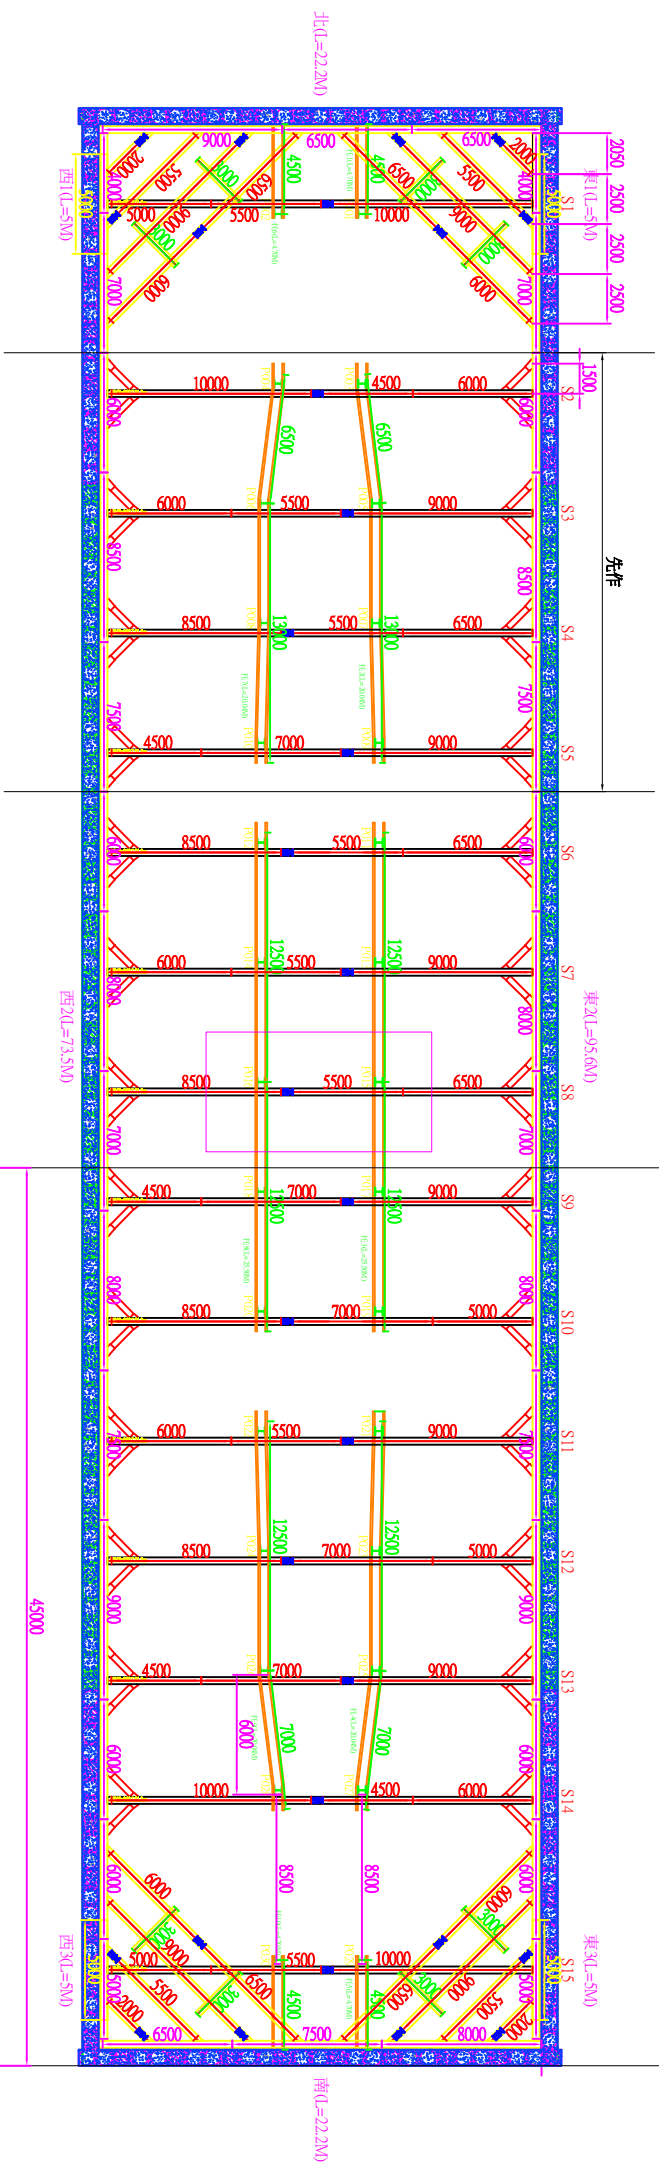

支撐大斜-H350*350*12*19
圍令-H350*350*12*19
托樑-C250
壓樑-C300